


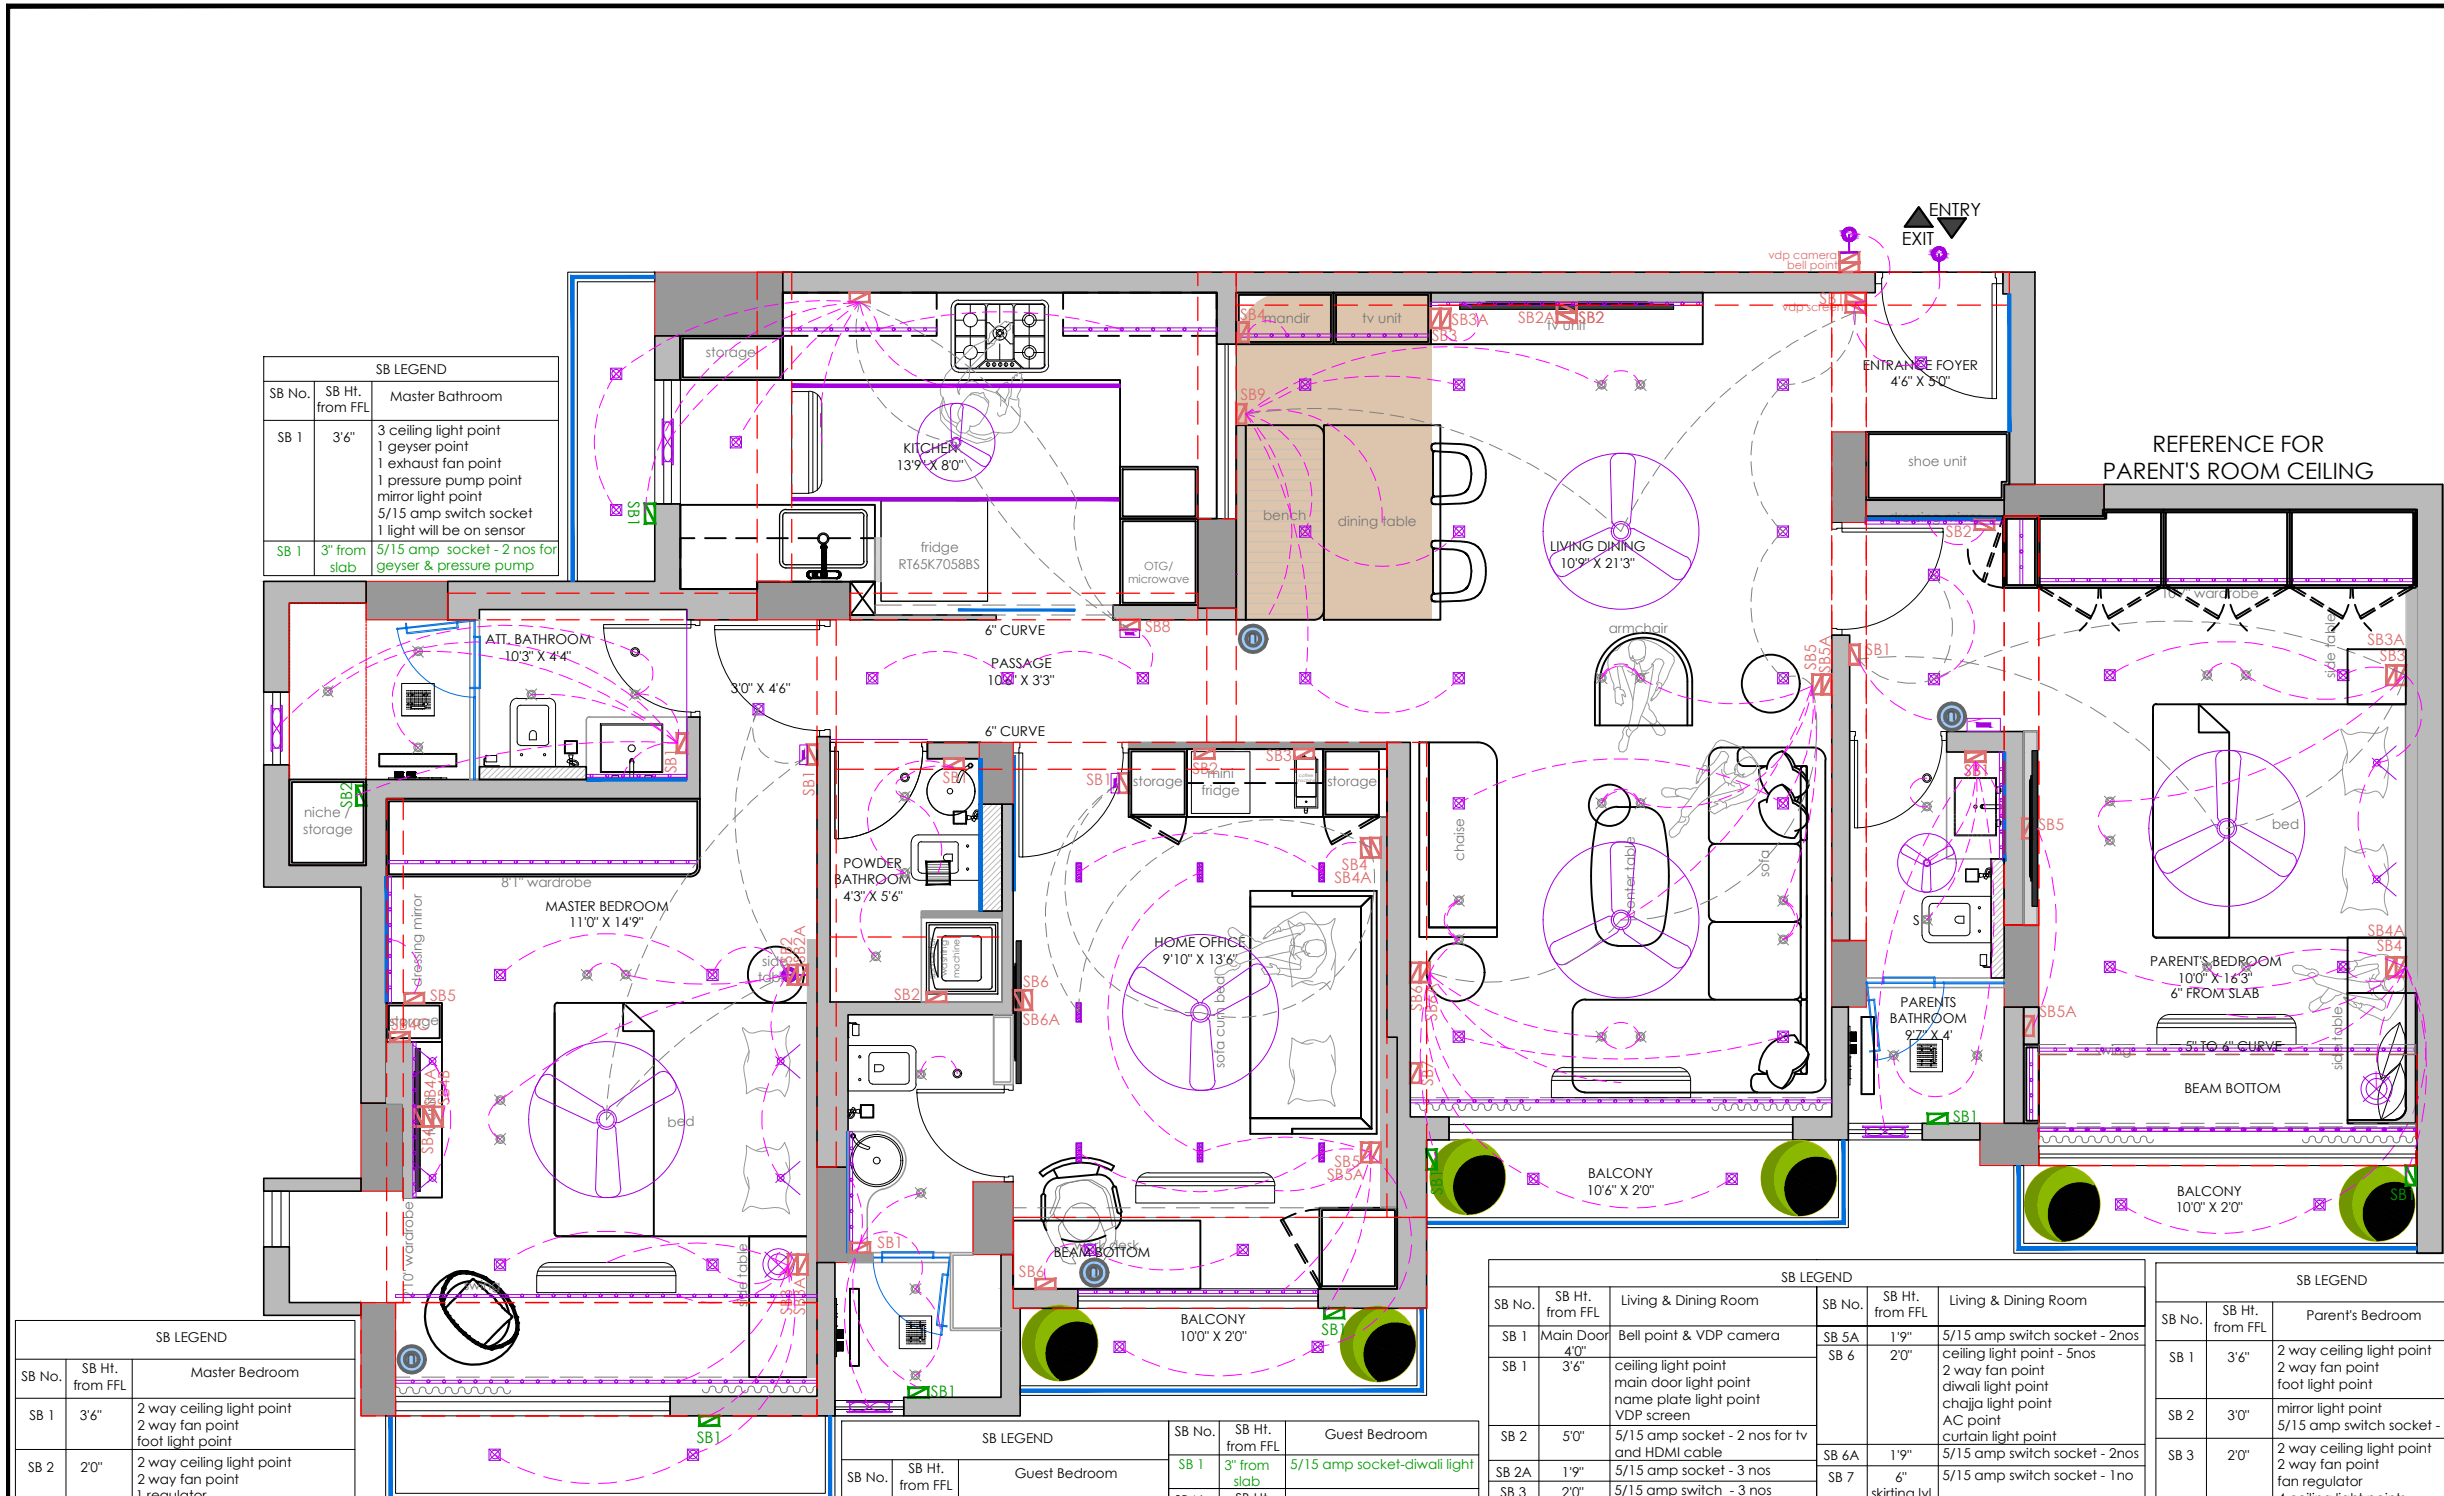

| SB LEGEND |                 |   |
|-----------|-----------------|---|
| SB No.    | SB Ht. from FFL | Master Bedroom   |
| SB 1      | 3'6"            | 2 way ceiling light point<br>2 way fan point<br>foot light point                                                                     |
| SB 2      | 2'0"            | 2 way ceiling light point<br>2 way fan point<br>1 regulator<br>4 ceiling light points                                                |
| SB 2A     | 1'9"            | 5/15 amp switch socket - 2 nos   |
| SB 3      | 2'0"            | 2 ceiling light points<br>AC point<br>curtain light point<br>chajja light point<br>diwali light point<br>hanging light point         |
| SB 3A     | 1'9"            | 5/15 amp switch socket - 2 nos   |
| SB 4      | 5'0"            | 5/15 amp socket - 2 nos for tv and HDMI cable                                                                                        |
| SB 4A     | 1'9"            | 5/15 amp socket - 3 nos   |
| SB 4A     | 2'0"            | 5/15 amp switches - 3 nos<br>switch for tv<br>sound bar switch<br>woofer switch<br>ceiling light point<br>panel indirect light point |
| SB 4B     | 1'3"            | 5/15 amp socket - 1 no for woofer   |
| SB 5      | 3'0"            | 5/15 amp switch socket - 2 nos<br>mirror light point                                                                                 |
| SB 1      | 3" from slab    | 5/15 amp socket-diwali light   |

| LIGHT LEGEND |                                              |        |                           |
|--------------|----------------------------------------------|--------|---------------------------|
| SYMBOL       | SPECIFICATIONS                               | SYMBOL | SPECIFICATIONS            |
|              | COB DOWN LIGHTER<br>DIMMABLE & TUNABLE - 15W |        | EXHAUST FAN               |
|              | LED PROFILE                                  |        | CEILING EXHAUST           |
|              | PROFILE LIGHTS LIGHT                         |        | 7 WATT COB                |
|              | CEILING FAN                                  |        | CAMERA                    |
|              | WIFI EXTENSION                               |        | SWITCH BOARD              |
|              | FOOT LIGHT                                   |        | WEATHERPROOF SWITCH BOARD |
|              | HANGING LIGHT                                |        | 2 WAY LOOPING             |
|              | WALL WASHER                                  |        | ONE WAY LOOPING           |
|              | WALL LIGHT POINT                             |        | SPLIT AC UNIT             |
|              | LIGHT SENSOR                                 |        |                           |

| SB LEGEND |                 |   |
|-----------|-----------------|---|
| SB No.    | SB Ht. from FFL | Guest Bedroom                                                                                         |
| SB 1      | 3'6"            | 2 way ceiling light point<br>2 way fan point<br>foot light point                                      |
| SB 2      | 1'9"            | 5/15 amp socket for mini fridge                                                                       |
| SB 3      | 3'0"            | 5/15 amp switch socket for coffee machine<br>Switch for mini fridge                                   |
| SB 4      | 2'0"            | 2 way ceiling light point<br>2 way fan point<br>ceiling light point                                   |
| SB 4A     | 2'0"            | 5/15 amp switch socket - 2 nos                                                                        |
| SB 5      | 2'0"            | 2 ceiling light points<br>AC point<br>curtain light point<br>chajja light point<br>diwali light point |
| SB 5A     | 3'0"            | 5/15 amp switch socket - 2 nos<br>ceiling light point                                                 |
| SB 6      | 5'0"            | 5/15 amp socket - 2 nos for tv and HDMI cable                                                         |
| SB 6A     | 2'0"            | 5/15 amp switch socket - 2 nos<br>switch for tv                                                       |

| SB LEGEND |                 |   |
|-----------|-----------------|---|
| SB No.    | SB Ht. from FFL | Guest Bedroom   |
| SB 1      | 3" from slab    | 5/15 amp socket-diwali light   |
| SB LEGEND |                 |   |
| SB No.    | SB Ht. from FFL | Guest Bathroom   |
| SB 1      | 3'6"            | 2 ceiling light point<br>1 geyser point<br>1 exhaust fan point<br>1 pressure pump point<br>mirror light point<br>5/15 amp switch socket<br>1 light will be on sensor |
| SB 1      | 3" from slab    | 5/15 amp socket - 2 nos for geyser & pressure pump   |

| SB LEGEND |                 |   |
|-----------|-----------------|---|
| SB No.    | SB Ht. from FFL | Living & Dining Room   |
| SB 1      | Main Door 4'0"  | Bell point & VDP camera   |
| SB 1      | 3'6"            | ceiling light point<br>main door light point<br>name plate light point<br>VDP screen   |
| SB 2      | 5'0"            | 5/15 amp socket - 2 nos for tv and HDMI cable   |
| SB 2A     | 1'9"            | 5/15 amp socket - 3 nos   |
| SB 3      | 2'0"            | 5/15 amp switch - 3 nos<br>switch for tv on/off - 1 no<br>sound bar switch - 1 no<br>woofer switch & extra - 2 nos                                                                      |
| SB 3A     | 6" skirting lvl | 5/15 amp socket - 2 nos for woofer & extra   |
| SB 4      | 3'0"            | 5/15 amp switch socket - 1 no<br>mandir light point   |
| SB 5      | 2'0"            | ceiling light point - 5 nos<br>2 way fan point<br>1 regulator   |
| SB LEGEND |                 |   |
| SB No.    | SB Ht. from FFL | Living & Dining Room   |
| SB 5A     | 1'9"            | 5/15 amp switch socket - 2 nos<br>ceiling light point - 5 nos<br>2 way fan point<br>foot light point                                                                                    |
| SB 6      | 2'0"            | 2 way fan point<br>diwali light point<br>chajja light point<br>AC point<br>curtain light point                                                                                          |
| SB 6A     | 1'9"            | 5/15 amp switch socket - 2 nos   |
| SB 7      | 6" skirting lvl | 5/15 amp switch socket - 1 no   |
| SB 8      | 3'6"            | ceiling light point - 1 no<br>foot light point<br>2 way kitchen light point<br>2 way kitchen fan point<br>ceiling light point - 6 nos<br>fan point                                      |
| SB 9      | 3'6"            | fan regulator<br>5/15 amp switch socket - 1 no   |
| SB 1      | 3" from slab    | 5/15 amp socket-diwali light   |
| SB LEGEND |                 |   |
| SB No.    | SB Ht. from FFL | Parent's Bedroom   |
| SB 1      | 3'6"            | 2 way ceiling light point<br>1 geyser point<br>1 exhaust fan point<br>1 pressure pump point<br>mirror light point<br>5/15 amp switch socket<br>1 fan point<br>1 light will be on sensor |
| SB 1      | 3" from slab    | 5/15 amp socket - 2 nos for geyser & pressure pump   |

| SB LEGEND |                 |   |
|-----------|-----------------|---|
| SB No.    | SB Ht. from FFL | Parent's Bedroom   |
| SB 1      | 3'6"            | 2 way ceiling light point<br>2 way fan point<br>foot light point                                                                                             |
| SB 2      | 3'0"            | mirror light point<br>5/15 amp switch socket - 1 no   |
| SB 3      | 2'0"            | 2 way ceiling light point<br>2 way fan point<br>fan regulator<br>4 ceiling light points                                                                      |
| SB 3A     | 2'0"            | 5/15 amp switch socket - 2 nos   |
| SB 4      | 2'0"            | 2 ceiling light points<br>AC point<br>curtain light point<br>ceiling indirect light point<br>chajja light point<br>diwali light point<br>hanging light point |
| SB 4A     | 2'0"            | 5/15 amp switch socket - 2 nos   |
| SB 5      | 5'0"            | 5/15 amp socket - 2 nos for tv and HDMI cable   |
| SB 5A     | 2'0"            | 5/15 amp switch socket - 2 nos<br>extra switch for tv   |
| SB 1      | 3" from slab    | 5/15 amp socket - for diwali light   |

## GENERAL NOTES

- All dimensions are in feet & inches and levels in feet unless specified otherwise.
- Do not scale the drawing; follow written dimensions.
- All dimensions are unfinished dimensions unless specified otherwise.
- Any discrepancies should be brought to the notice of the Architect prior to execution of job / procuring materials at site.
- This drawing is the property of AS Architects and should not be reproduced, copied, handed over to a third party or used for any purpose other than for which it has been issued.
- This drawing is to be read in conjunction with all relevant structural & services drawings.
- The Contractor shall verify all existing dimensions and site conditions prior to commencing work or fabrication and shall immediately notify the Architect of any variance from the drawings.
- All work shall be executed in accordance with the specifications, which shall take precedence over the drawings regarding material type, quality, and installation standards.

## REVISIONS

| SR. NO. | AMENDMENTS | BY | DATE |
|---------|------------|----|------|
|         |            |    |      |
|         |            |    |      |
## CLIENT:-

MR. YOGESH DEDHIA

## SITE ADDRESS:-

C/503, Gokul Divine, Irla S.V. road, Vile Parle West, Mumbai 400056

## STAMP & SIGN



|                                                  |                |
|--------------------------------------------------|----------------|
| PROJECT TITLE                                    | PROJ. NO.      |
| <b>GOKUL DIVINE</b><br>VILE PARLE (WEST), MUMBAI | AS/26/1-RES/05 |

|               |        |
|---------------|--------|
| DRAWING TITLE | DWG.NO |
|---------------|--------|

|                                   |    |
|-----------------------------------|----|
| <b>PROPOSED ELECTRICAL LAYOUT</b> | 01 |
|-----------------------------------|----|

|               |        |
|---------------|--------|
| DRAWING STAGE | REV.NO |
|---------------|--------|

## DISCUSSION DRAWING

|          |            |       |            |
|----------|------------|-------|------------|
| DRAWN BY | CHECKED BY | SCALE | DATE       |
|          |            | NTS   | 03/07/2026 |



**AS ARCHITECTS**

Address: 103/C, Thosar House, Hanuman cross road no.1, Near Shivveela hotel, Vile Parle (East), Mumbai-400057.  
Phone: +91-9930969337  
E-mail: [info@asarchitects.co.in](mailto:info@asarchitects.co.in)  
Website: [www.asarchitects.co.in](http://www.asarchitects.co.in)