


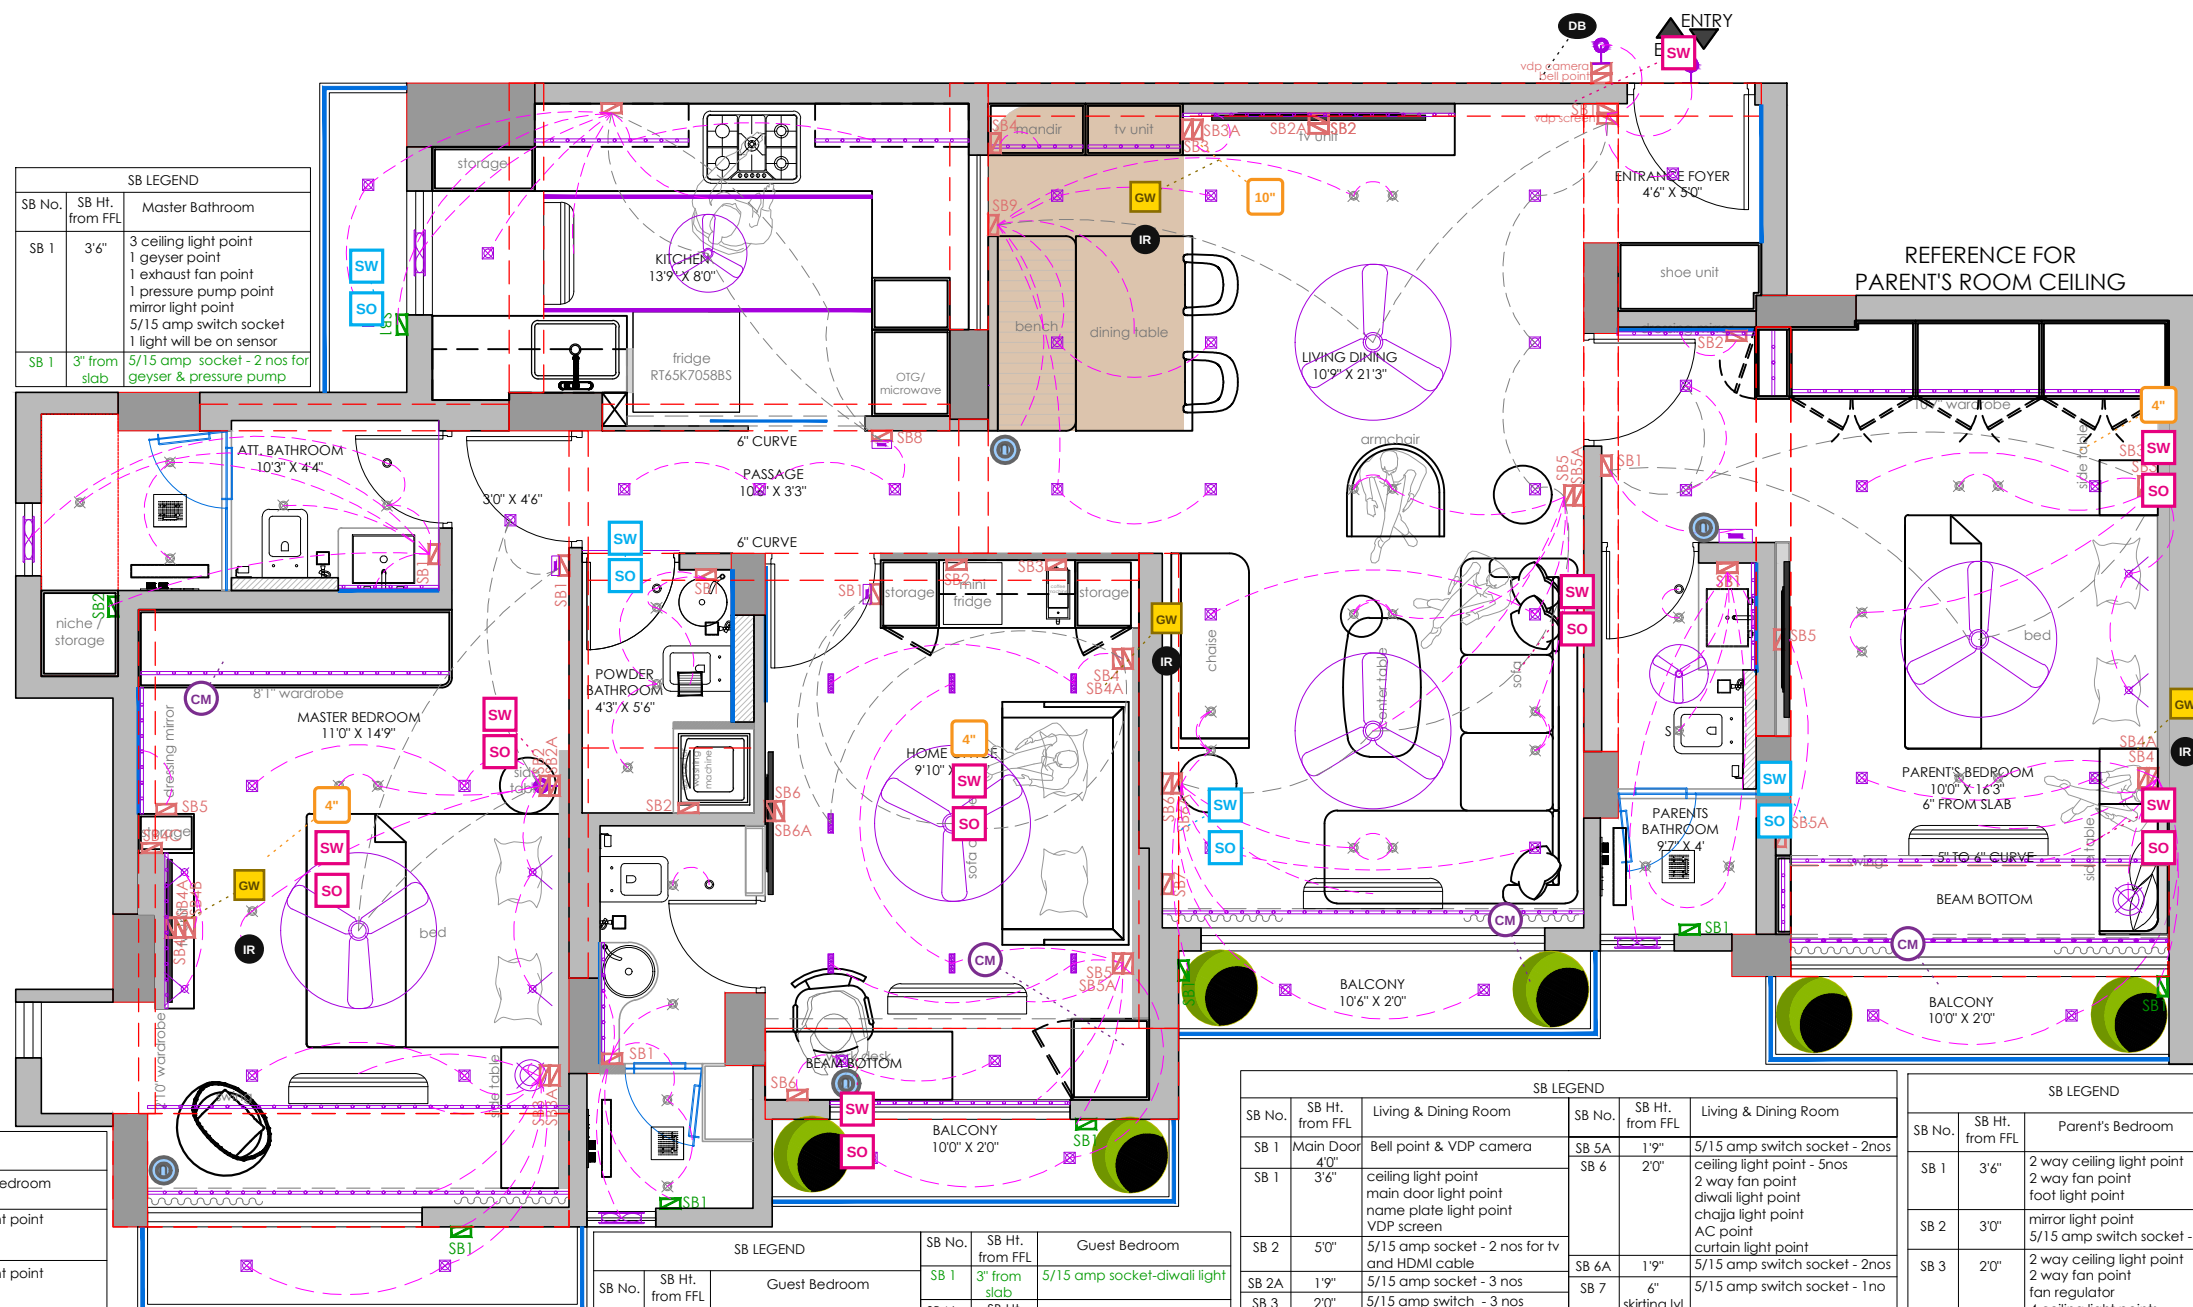

SB LEGEND		
SB No.	SB Ht. from FFL	Master Bedroom
SB 1	3'6"	3 ceiling light point 1 geyser point 1 exhaust fan point 1 pressure pump point mirror light point 5/15 amp switch socket 1 light will be on sensor
SB 1	3" from slab	5/15 amp socket - 2 nos for geyser & pressure pump

SB LEGEND		
SB No.	SB Ht. from FFL	Master Bedroom
SB 1	3'6"	2 way ceiling light point 2 way fan point foot light point
SB 2	2'0"	2 way ceiling light point 2 way fan point 1 regulator 4 ceiling light points
SB 2A	1'9"	5/15 amp switch socket - 2 nos
SB 3	2'0"	2 ceiling light points AC point curtain light point chajja light point diwali light point hanging light point
SB 3A	1'9"	5/15 amp switch socket - 2 nos
SB 4	5'0"	5/15 amp socket - 2 nos for tv and HDMI cable
SB 4A	1'9"	5/15 amp socket - 3 nos
SB 4A	2'0"	5/15 amp switches - 3 nos switch for tv sound bar switch woofer switch ceiling light point panel indirect light point
SB 4B	1'3"	5/15 amp socket - 1 no for woofer
SB 5	3'0"	5/15 amp switch socket - 2 nos mirror light point
SB 1	3" from slab	5/15 amp socket-diwali light

LIGHT LEGEND			
SYMBOL	SPECIFICATIONS	SYMBOL	SPECIFICATIONS
	COB DOWN LIGHTER DIMMABLE & TUNABLE -15W		EXHAUST FAN
	LED PROFILE		CEILING EXHAUST
	PROFILE LIGHTS LIGHT		7 WATT COB
	CEILING FAN		CAMERA
	WIFI EXTENSION		SWITCH BOARD
	FOOT LIGHT		WEATHERPROOF SWITCH BOARD
	HANGING LIGHT		2 WAY LOOPING
	WALL WASHER		ONE WAY LOOPING
	WALL LIGHT POINT		SPLIT AC UNIT
	LIGHT SENSOR		

SB LEGEND		
SB No.	SB Ht. from FFL	Guest Bedroom
SB 1	3'6"	2 way ceiling light point 2 way fan point foot light point
SB 2	1'9"	5/15 amp socket for mini fridge
SB 3	3'0"	5/15 amp switch socket for coffee machine Switch for mini fridge
SB 4	2'0"	2 way ceiling light point 2 way fan point ceiling light point
SB 4A	2'0"	5/15 amp switch socket - 2 nos
SB 5	2'0"	2 ceiling light points AC point curtain light point chajja light point diwali light point
SB 5A	3'0"	5/15 amp switch socket - 2 nos ceiling light point
SB 6	5'0"	5/15 amp socket - 2 nos for tv and HDMI cable
SB 6A	2'0"	5/15 amp switch socket - 2 nos switch for tv

SB LEGEND		
SB No.	SB Ht. from FFL	Guest Bedroom
SB 1	3" from slab	5/15 amp socket-diwali light
SB LEGEND		
SB No.	SB Ht. from FFL	Guest Bathroom
SB 1	3'6"	2 ceiling light point 1 geyser point 1 exhaust fan point 1 pressure pump point mirror light point 5/15 amp switch socket 1 light will be on sensor
SB 1	3" from slab	5/15 amp socket - 2 nos for geyser & pressure pump

SB LEGEND		
SB No.	SB Ht. from FFL	Living & Dining Room
SB 1	Main Door 4'0"	Bell point & VDP camera
SB 1	3'6"	ceiling light point main door light point name plate light point VDP screen
SB 2	5'0"	5/15 amp socket - 2 nos for tv and HDMI cable
SB 2A	1'9"	5/15 amp socket - 3 nos
SB 3	2'0"	5/15 amp switch - 3 nos switch for tv on/off - 1 no sound bar switch - 1 no woofer switch & extra - 2 nos
SB 3A	6" skirting lvl	5/15 amp switch socket - 2 nos for woofer & extra
SB 4	3'0"	5/15 amp switch socket - 1 no mandir light point
SB 5	2'0"	ceiling light point - 5 nos 2 way fan point 1 regulator
SB LEGEND		
SB No.	SB Ht. from FFL	Living & Dining Room
SB 5A	1'9"	5/15 amp switch socket - 2 nos ceiling light point - 5 nos 2 way fan point foot light point
SB 6	2'0"	2 way fan point diwali light point chajja light point AC point curtain light point
SB 6A	1'9"	5/15 amp switch socket - 2 nos
SB 7	6" skirting lvl	5/15 amp switch socket - 1 no
SB 8	3'6"	ceiling light point - 1 no foot light point 2 way kitchen light point 2 way kitchen fan point ceiling light point - 6 nos fan point
SB 9	3'6"	fan regulator 5/15 amp switch socket - 1 no
SB 1	3" from slab	5/15 amp socket-diwali light
SB LEGEND		
SB No.	SB Ht. from FFL	Parent's Bedroom
SB 1	3'6"	2 way ceiling light point 1 geyser point 1 exhaust fan point 1 pressure pump point mirror light point 5/15 amp switch socket 1 fan point 1 light will be on sensor
SB 1	3" from slab	5/15 amp socket - 2 nos for geyser & pressure pump

SB LEGEND		
SB No.	SB Ht. from FFL	Parent's Bedroom
SB 1	3'6"	2 way ceiling light point 2 way fan point foot light point
SB 2	3'0"	mirror light point 5/15 amp switch socket - 1 no
SB 3	2'0"	2 way ceiling light point 2 way fan point fan regulator 4 ceiling light points
SB 3A	2'0"	5/15 amp switch socket - 2 nos
SB 4	2'0"	2 ceiling light points AC point curtain light point ceiling indirect light point chajja light point diwali light point hanging light point
SB 4A	2'0"	5/15 amp switch socket - 2 nos
SB 5	5'0"	5/15 amp socket - 2 nos for tv and HDMI cable
SB 5A	2'0"	5/15 amp switch socket - 2 nos extra switch for tv
SB 1	3" from slab	5/15 amp socket - for diwali light

PRODUCT TOTALS (this proposal) — SW:12 SO:11 4":3 10":1 CM:4 GW:4 IR:4 DB:1 cameras:0

PROPOSED / FOR REVIEW / NOT FOR EXECUTION

viwaves automation overlay — base-only discussion drawing — Cursor cloud marking check 2026-09-24

OVERLAY LEGEND (viwaves simplified family)

SW — switch (magenta = on wall, cyan = wall bracket) (qty 12)
SO — socket (magenta = on wall, cyan = wall bracket) (qty 11)
4" — bedside/secondary touch screen (qty 3)
10" — living/central touch screen (qty 1)
CM — curtain motor (candidate drive end) (qty 4)
GW — surface gateway (qty 4)
IR — IR blaster (separate from GW) (qty 4)
DB — doorbell / VDP badge (qty 1)
Cameras: 0 (not scoped on this base)

GENERAL NOTES

- All dimensions are in feet & inches and levels in feet unless specified otherwise.
- Do not scale the drawing; follow written dimensions.
- All dimensions are unfinished dimensions unless specified otherwise.
- Any discrepancies should be brought to the notice of the Architect prior to execution of job / procuring materials at site.
- This drawing is the property of AS Architects and should not be reproduced, copied, handed over to a third party or used for any purpose other than for which it has been issued.
- This drawing is to be read in conjunction with all relevant structural & services drawings.
- The Contractor shall verify all existing dimensions and site conditions prior to commencing work or fabrication and shall immediately notify the Architect of any variance from the drawings.
- All work shall be executed in accordance with the specifications, which shall take precedence over the drawings regarding material type, quality, and installation standards.

REVISIONS

SR. NO.	AMENDMENTS	BY	DATE

CLIENT:-

MR. YOGESH DEDHIA

SITE ADDRESS:-

C/503, Gokul Divine, Irla S.V. road, Vile Parle West, Mumbai 400056

STAMP & SIGN



PROJECT TITLE	PROJ. NO.
GOKUL DIVINE VILE PARLE (WEST), MUMBAI	AS/26/I-RES/05

DRAWING TITLE	DWG.NO
---------------	--------

PROPOSED ELECTRICAL LAYOUT	01
-----------------------------------	----

DRAWING STAGE	REV.NO
---------------	--------

DISCUSSION DRAWING

DRAWN BY	CHECKED BY	SCALE	DATE
		NTS	03/07/2026



Address: 103/C, Thosar House, Hanuman cross road no.1, Near Shivveela hotel, Vile Parle (East), Mumbai-400057.
Phone: +91-9930969337
E-mail: info@asarchitects.co.in
Website: www.asarchitects.co.in